


Zorzal 2 - topografía preliminar reproducible

Catastro 7923502VK0072S + MDT02-ETRS89-HU30-0657-1-COB2.tif (2019) | ETRS89 / UTM 30N | Análisis preliminar

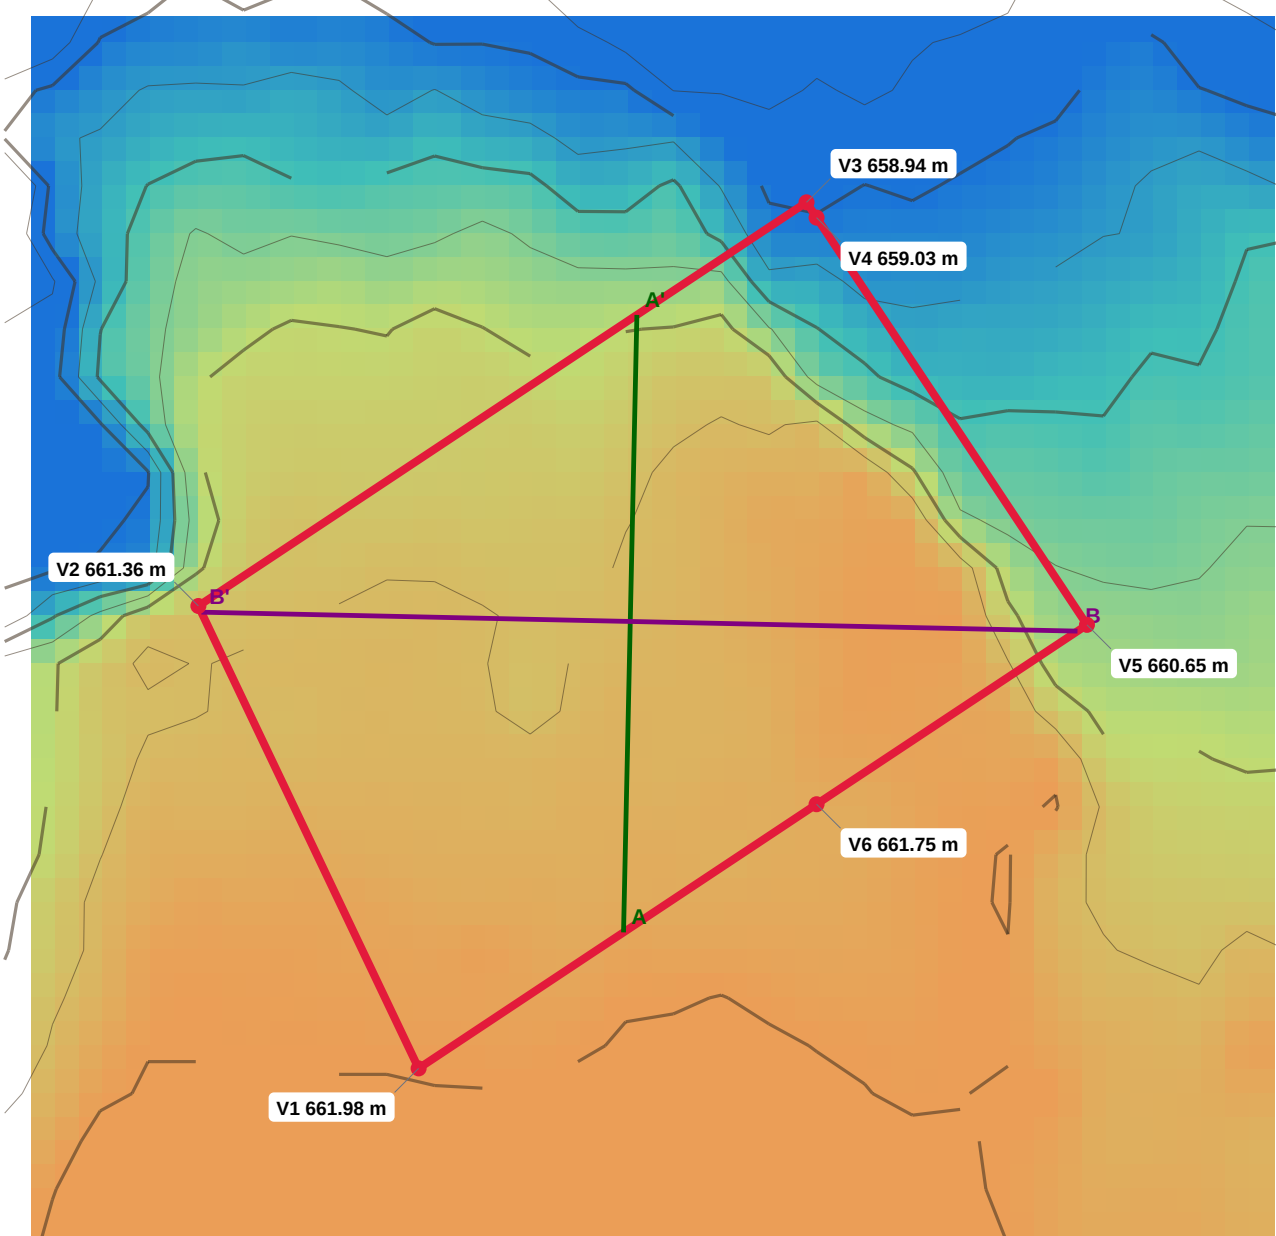

Cota MDT02



Resultado dentro de parcela

Superficie Catastro	681 m ²
Superficie geométrica	680.77 m ²
Cota mínima / máxima	658.98 / 661.96 m
Desnivel total	2.98 m
Pendiente plano ajustado	4.5 %
Dirección de bajada	1° (desde norte)
Longitud A-A'	25.86 m
Desnivel A-A'	0.94 m
Pendiente A-A'	3.6 %

Lectura técnica

La parcela desciende principalmente hacia el N.

El desnivel estimado debe contrastarse con la rasante real de calle, bordillos, acometidas y linderos.

Las cotas proceden de una malla pública interpolada de 2 m: sirven para criba, no para proyecto de obra.

No se ha aplicado suavizado adicional al MDT02.


La fachada/calle debe confirmarse sobre ortofoto, catastro y levantamiento antes de la implantación.




Perfiles topográficos de la parcela

Catastro 7923502VK0072S + MDT02-ETRS89-HU30-0657-1-COB2.tif (2019) | ETRS89 / UTM 30N | Análisis preliminar

A-A' - máxima pendiente ajustada

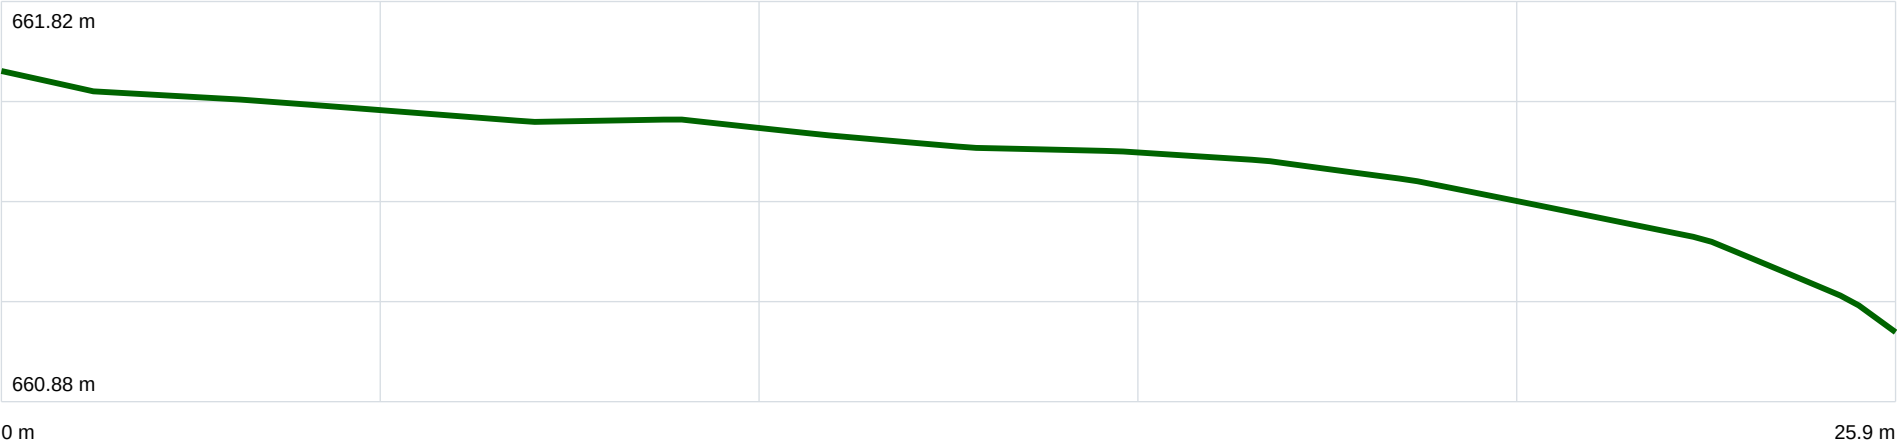

B-B' - sección transversal

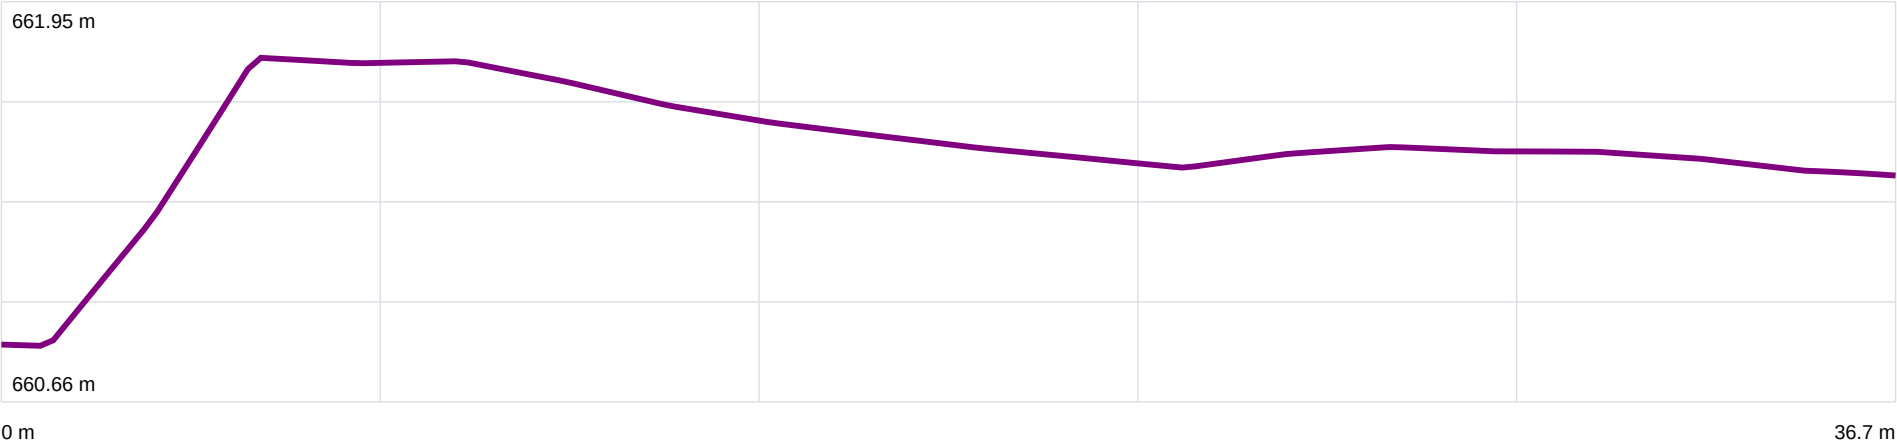

Perfiles muestreados cada 0,25 m mediante interpolación bilineal del MDT02. La precisión aparente de los decimales no equivale a precisión topográfica. La línea A-A' se calcula desde el plano de mejor ajuste a todas las muestras interiores; B-B' es perpendicular y pasa por el centroide.