


# Alcotán 20 - topografía preliminar reproducible

Catastro 8029308VK0082N + MDT02-ETRS89-HU30-0657-1-COB2.tif (2019) | ETRS89 / UTM 30N | Análisis preliminar

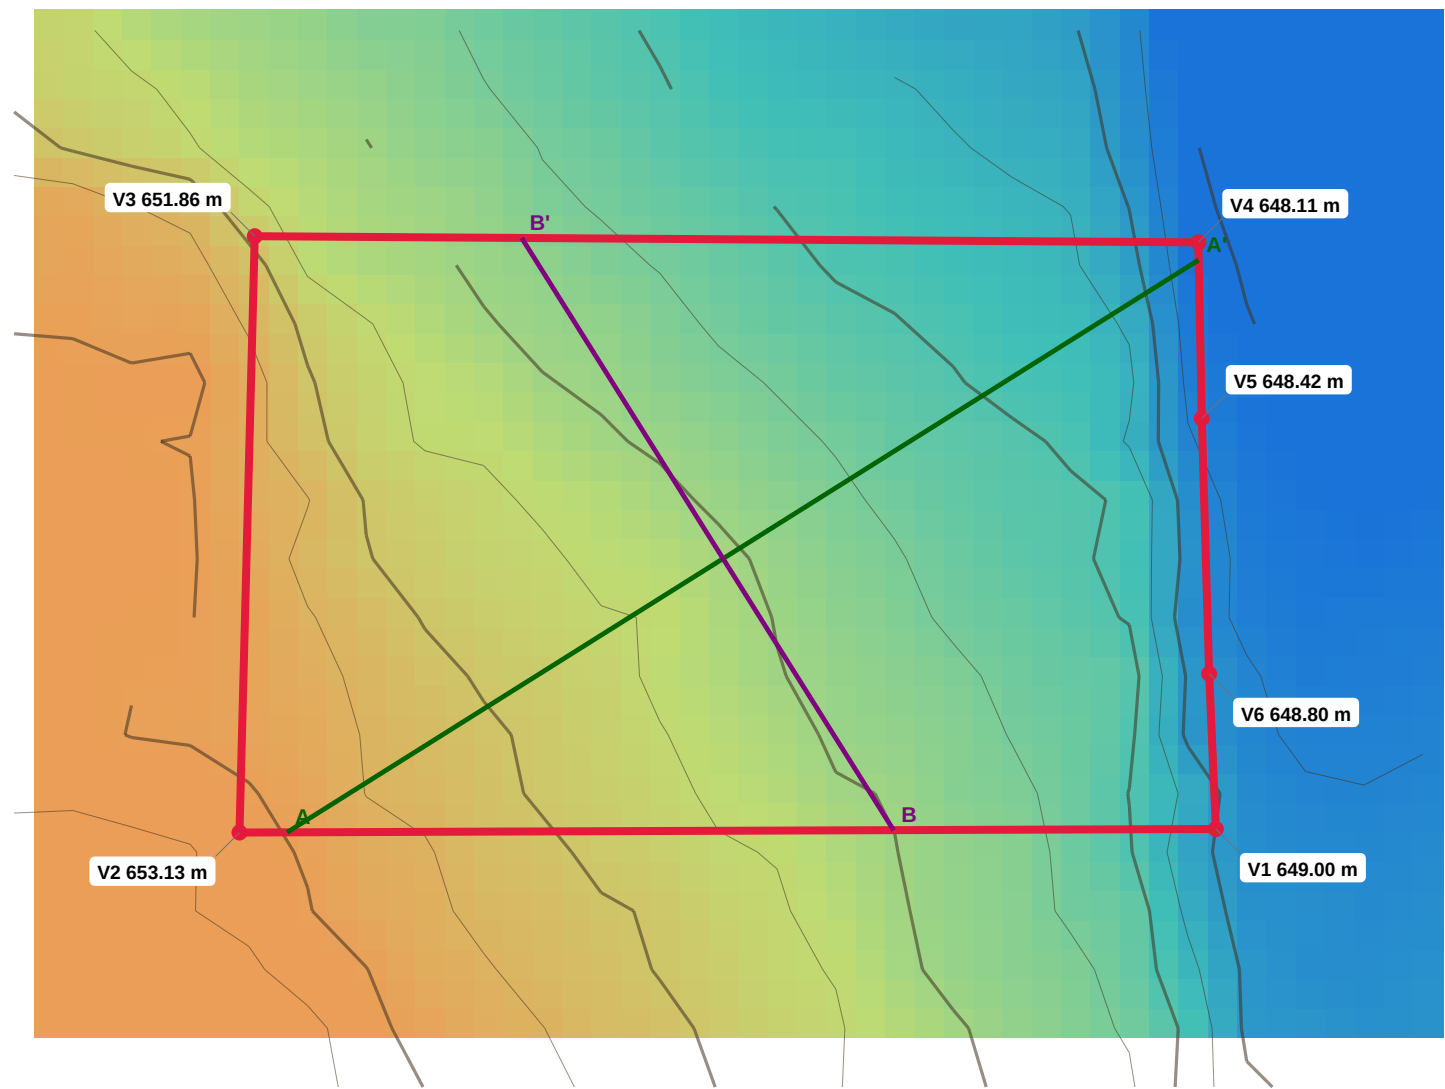

## Cota MDT02



## Resultado dentro de parcela

|                        |                       |
|------------------------|-----------------------|
| Superficie Catastro    | 658 m <sup>2</sup>    |
| Superficie geométrica  | 658.33 m <sup>2</sup> |
| Cota mínima / máxima   | 648.13 / 653.04 m     |
| Desnivel total         | 4.91 m                |
| Pendiente media local  | 14.3 %                |
| Pendiente p95 / máxima | 35.1 / 40.4 %         |
| Dirección de bajada    | 58° (desde norte)     |
| Longitud A-A'          | 36.67 m               |
| Desnivel A-A'          | 4.84 m                |
| Pendiente A-A'         | 13.2 %                |

## Lectura técnica

La parcela desciende principalmente hacia el NE.

El desnivel estimado debe contrastarse con la rasante real de calle, bordillos, acometidas y linderos.

Las cotas proceden de una malla pública interpolada de 2 m: sirven para criba, no para proyecto de obra.

No se ha aplicado suavizado adicional al MDT02.


La fachada/calle debe confirmarse sobre ortofoto, catastro y levantamiento antes de la implantación.




# Perfiles topográficos de la parcela

Catastro 8029308VK0082N + MDT02-ETRS89-HU30-0657-1-COB2.tif (2019) | ETRS89 / UTM 30N | Análisis preliminar

A-A' - máxima pendiente ajustada

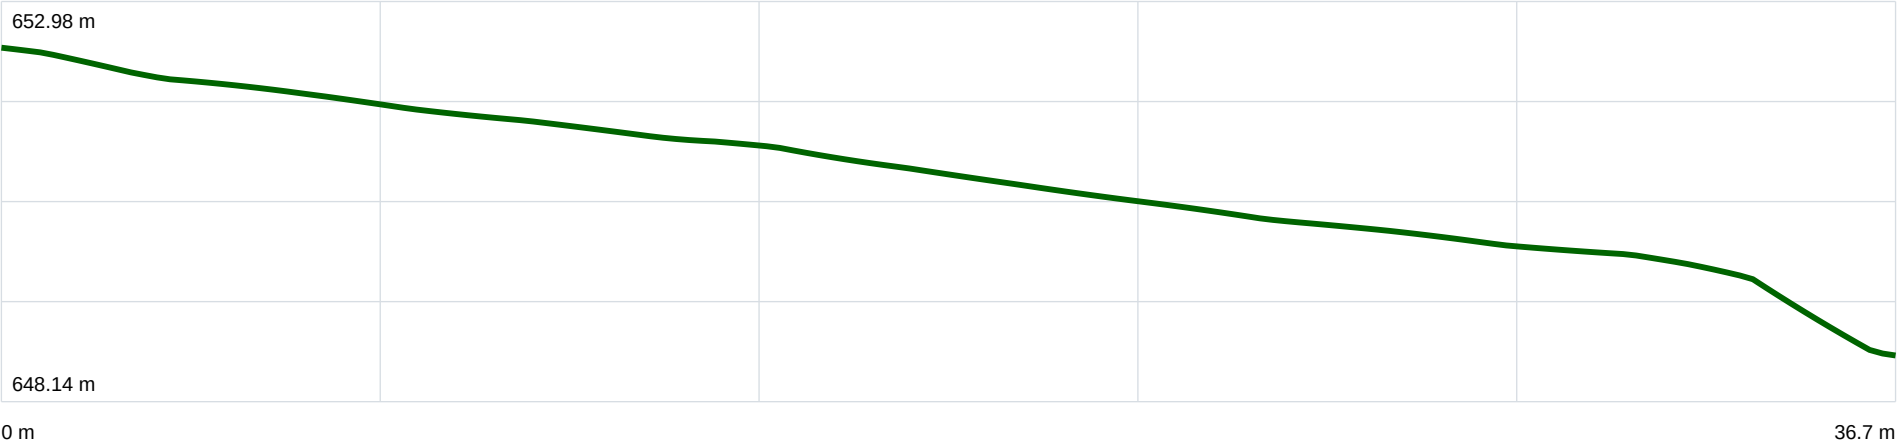

B-B' - sección transversal

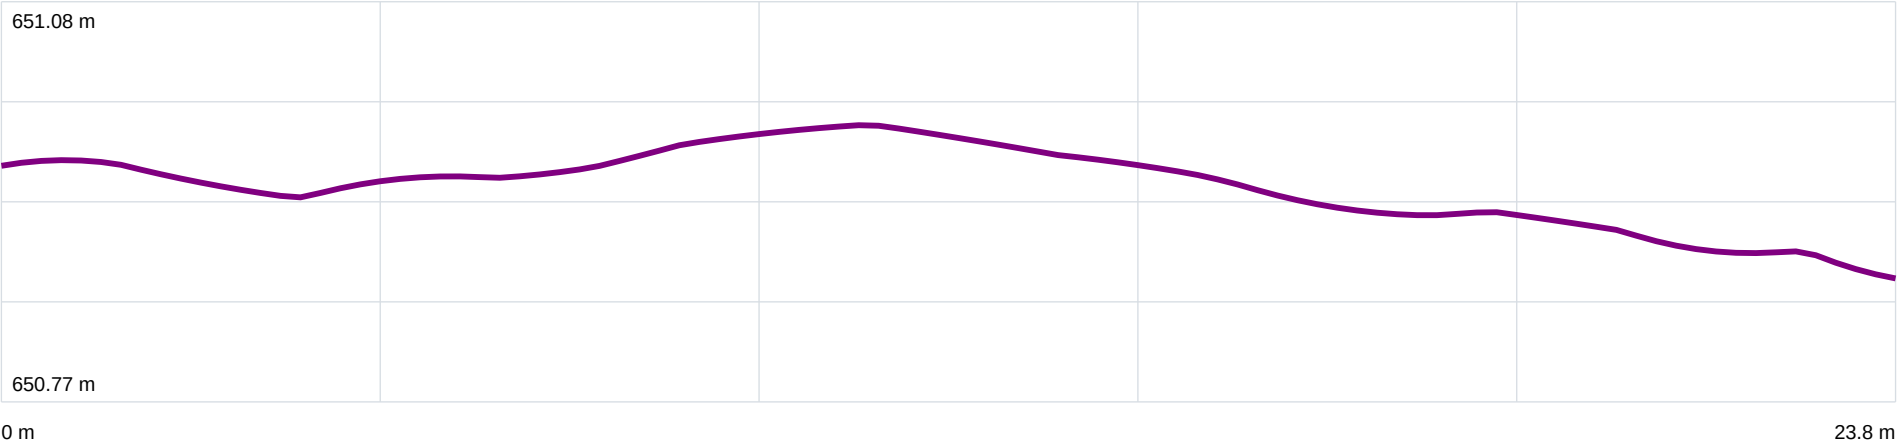

Perfiles muestreados cada 0,25 m mediante interpolación bilineal del MDT02. La precisión aparente de los decimales no equivale a precisión topográfica.  
La línea A-A' se calcula desde el plano de mejor ajuste a todas las muestras interiores; B-B' es perpendicular y pasa por el centroide.