


Alcotán 29 - topografía preliminar reproducible

Catastro 8028615VK0082N + MDT02-ETRS89-HU30-0657-1-COB2.tif (2019) | ETRS89 / UTM 30N | Análisis preliminar

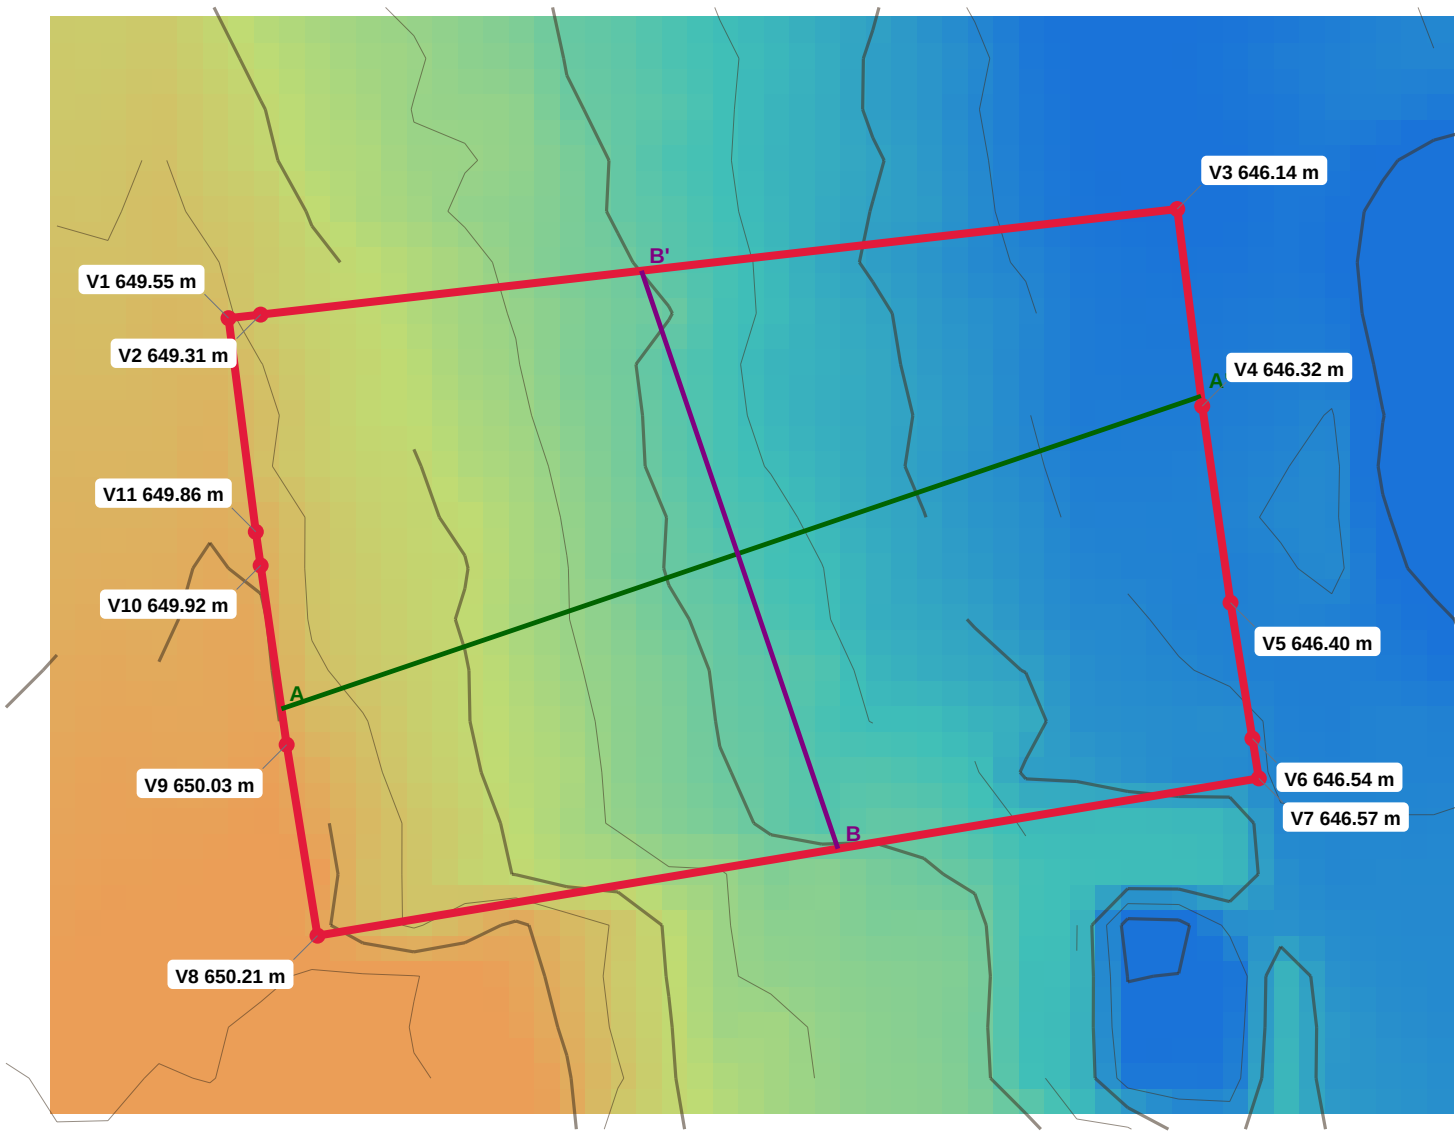

Cota MDT02



Resultado dentro de parcela

Superficie Catastro	880 m²
Superficie geométrica	880.39 m²
Cota mínima / máxima	646.15 / 650.29 m
Desnivel total	4.14 m
Pendiente media local	10.6 %
Pendiente p95 / máxima	18.6 / 28.8 %
Dirección de bajada	71° (desde norte)
Longitud A-A'	38.09 m
Desnivel A-A'	3.65 m
Pendiente A-A'	9.6 %

Lectura técnica

La parcela desciende principalmente hacia el E.

El desnivel estimado debe contrastarse con la rasante real de calle, bordillos, acometidas y linderos.

Las cotas proceden de una malla pública interpolada de 2 m: sirven para criba, no para proyecto de obra.

No se ha aplicado suavizado adicional al MDT02.


La fachada/calle debe confirmarse sobre ortofoto, catastro y levantamiento antes de la implantación.




Perfiles topográficos de la parcela

Catastro 8028615VK0082N + MDT02-ETRS89-HU30-0657-1-COB2.tif (2019) | ETRS89 / UTM 30N | Análisis preliminar

A-A' - máxima pendiente ajustada

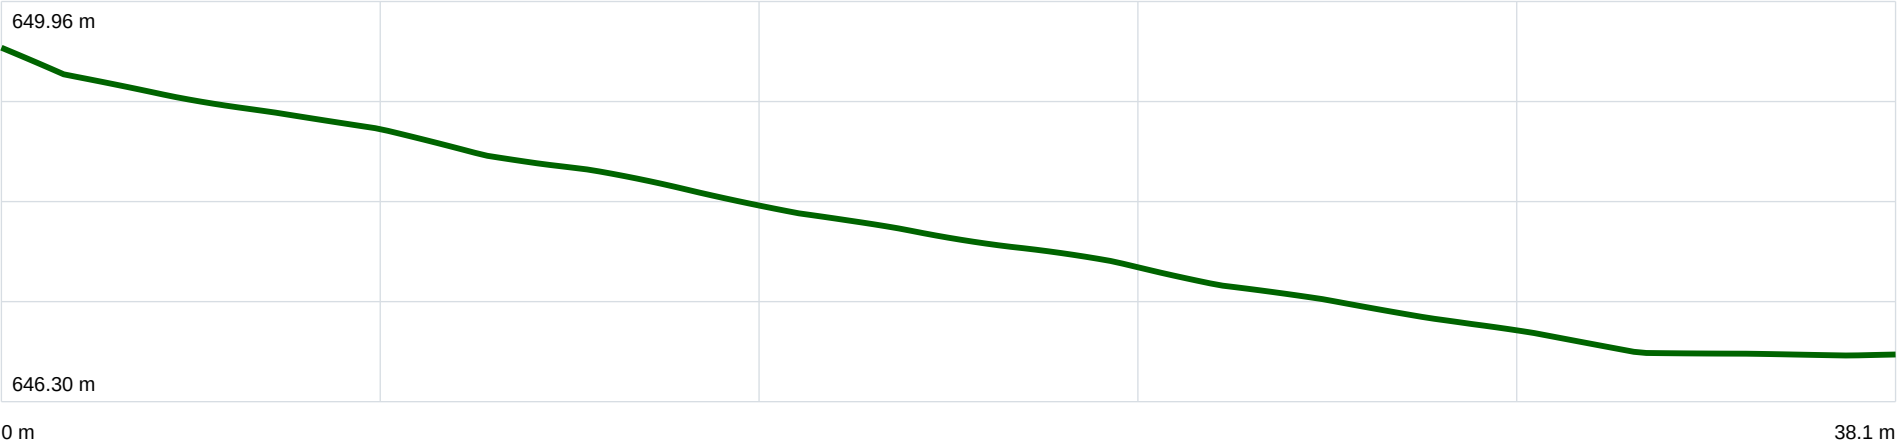

B-B' - sección transversal

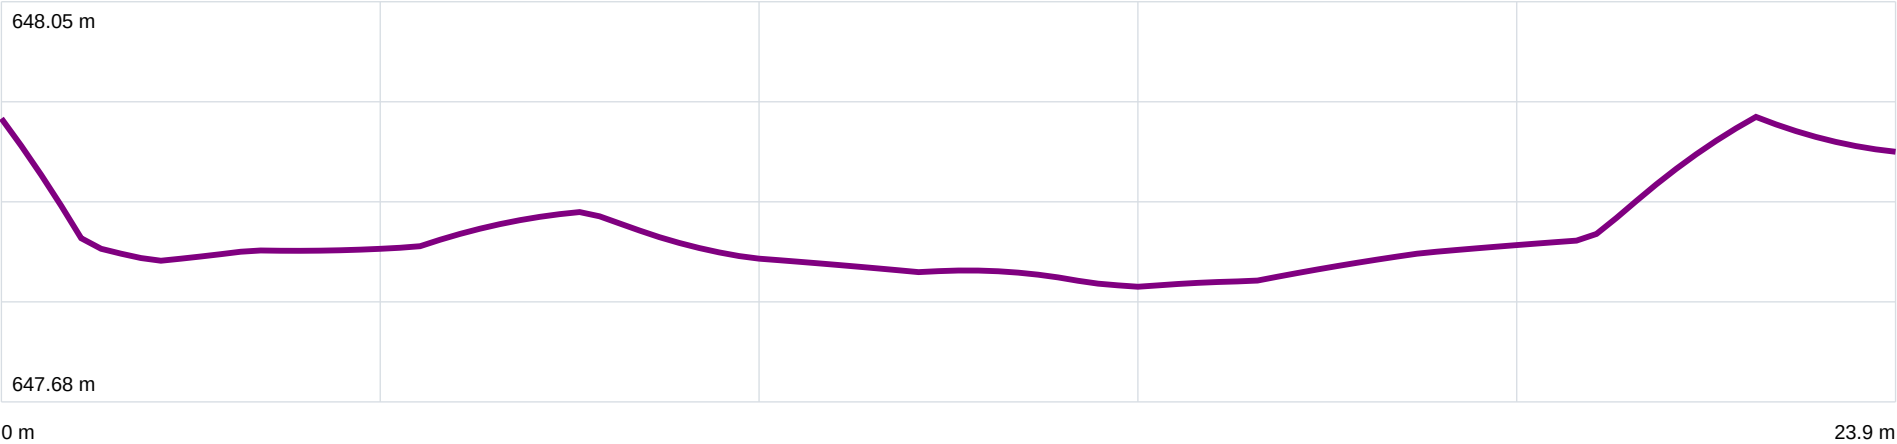

Perfiles muestreados cada 0,25 m mediante interpolación bilineal del MDT02. La precisión aparente de los decimales no equivale a precisión topográfica. La línea A-A' se calcula desde el plano de mejor ajuste a todas las muestras interiores; B-B' es perpendicular y pasa por el centroide.